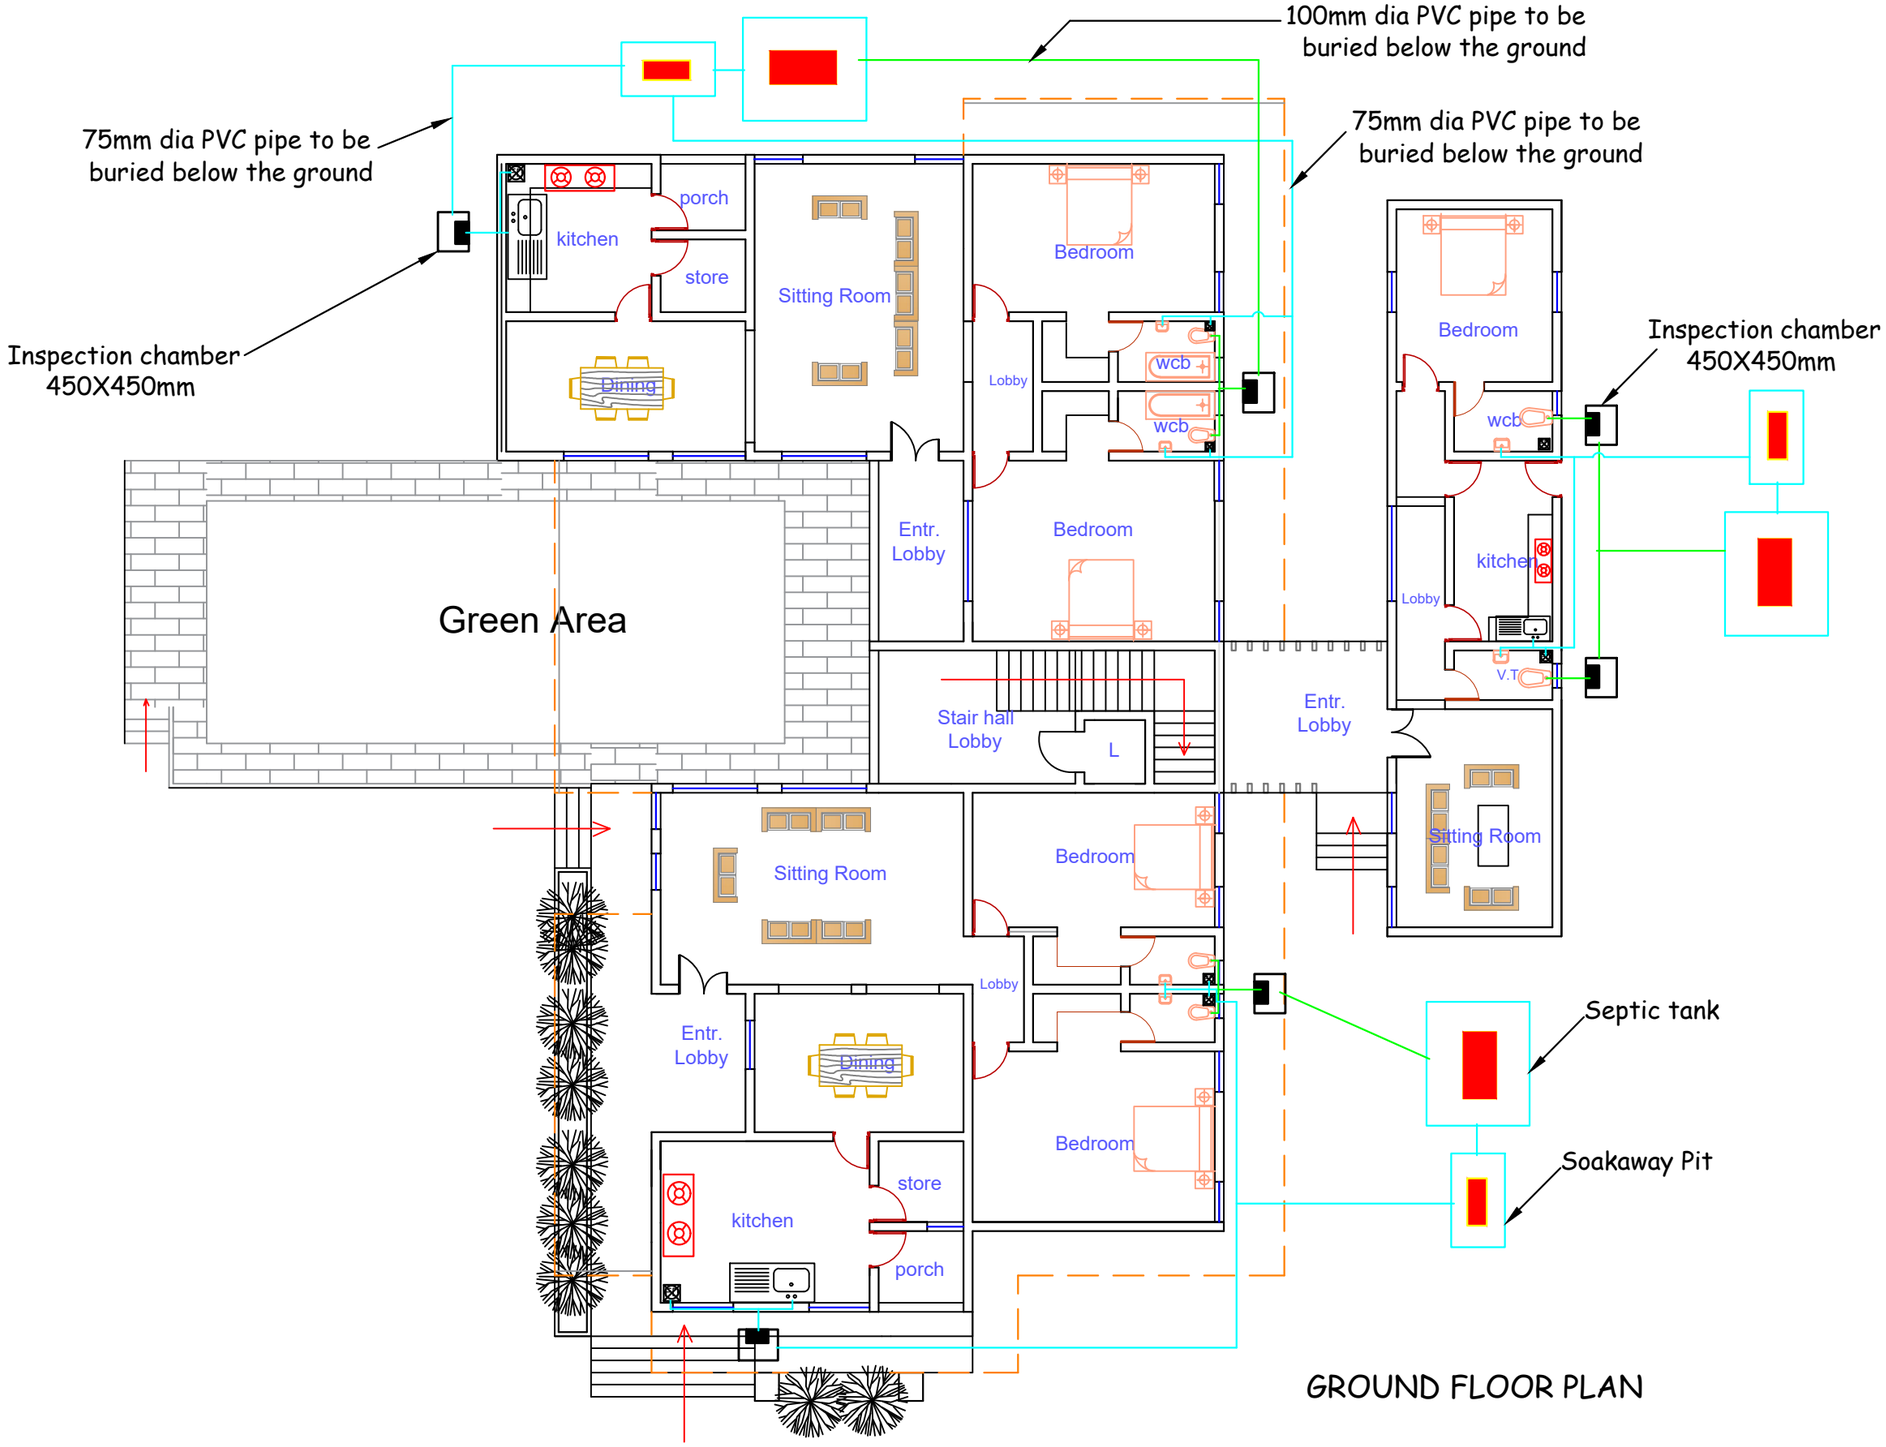

GROUND FLOOR PLAN

Project	Location	Client		Scale	Design	Drawing Title		Stamp
PROPOSED RESIDENTIAL DEVELOPMENT	JAHI/B08/2423 F.C.T, ABUJA.	ALHAJI SANUSI ABUBAKAR	BIGAFOM VENTURES ELECTRICAL & MECHANICAL ENGINEERS PLOT 11 BLOCK D. PASTOR EJIDE ALADESIAYE CRESCENT ODA COMMUNITY ESTATE PHASE 2 ODA, AKURE SOUTH LOCAL GOVERNMENT AREA, ONDO STATE. 08038361849 bigafom@yahoo.com bigafom@gmail.com	NTS	Engr. O.J Arowosafe	Soil And Waste Layout	ME 01	
				Date Sep. 2021	Checked Engr. B.A.			